




ST. CLAIR COLLEGE

Civil Engineering
Technology



No.	Revision / Issue
1	Bath Insulation Added
2	North Arrow Added
3	Hatch Corrected

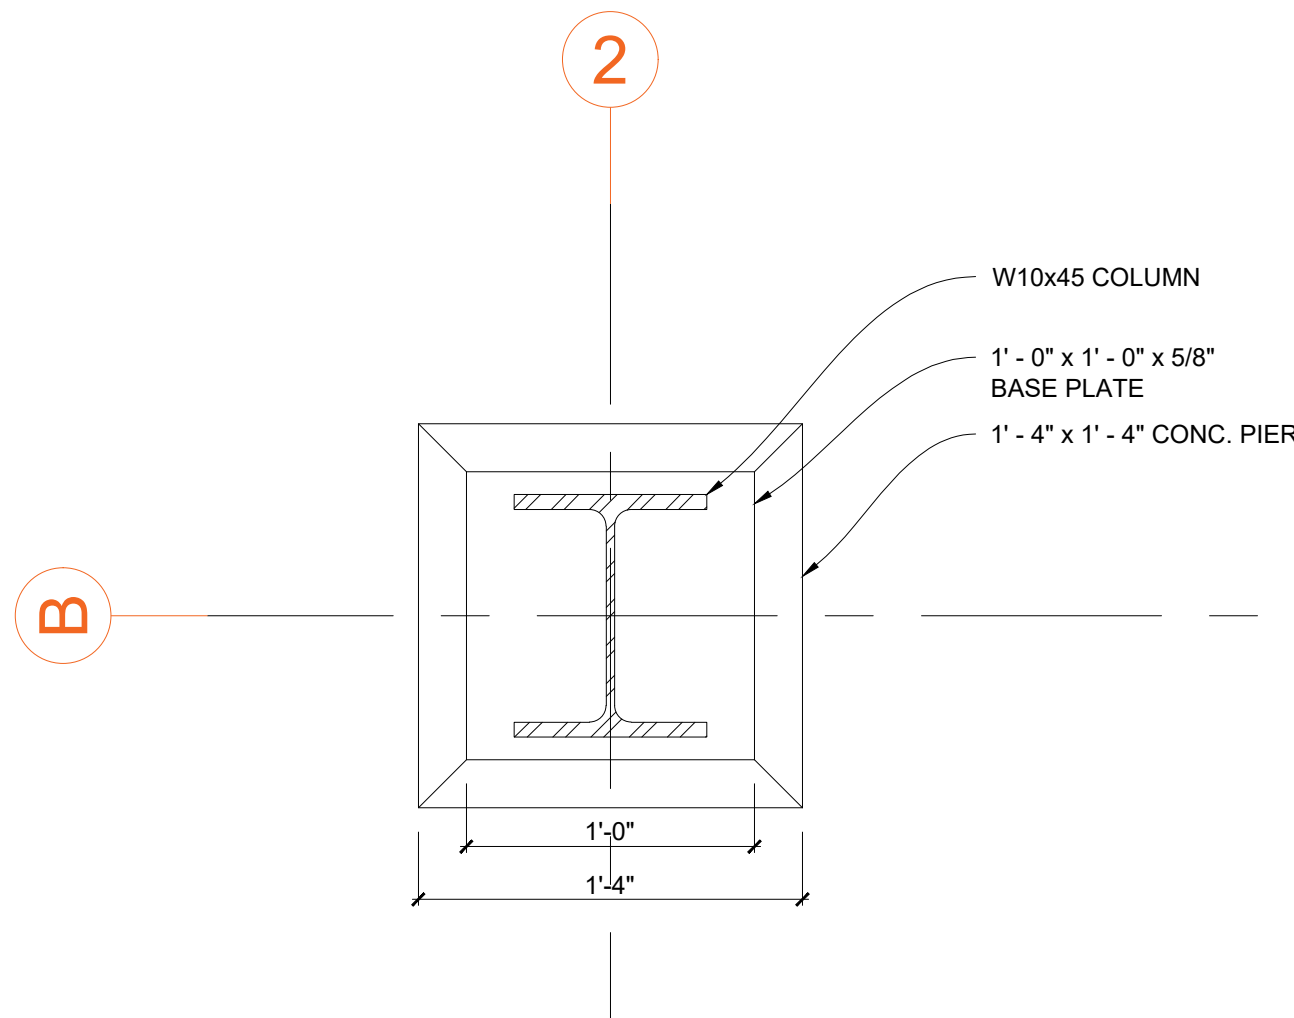


2 COLUMN B2 DETAIL
SCALE: 1 - 1/2" = 1' - 0"

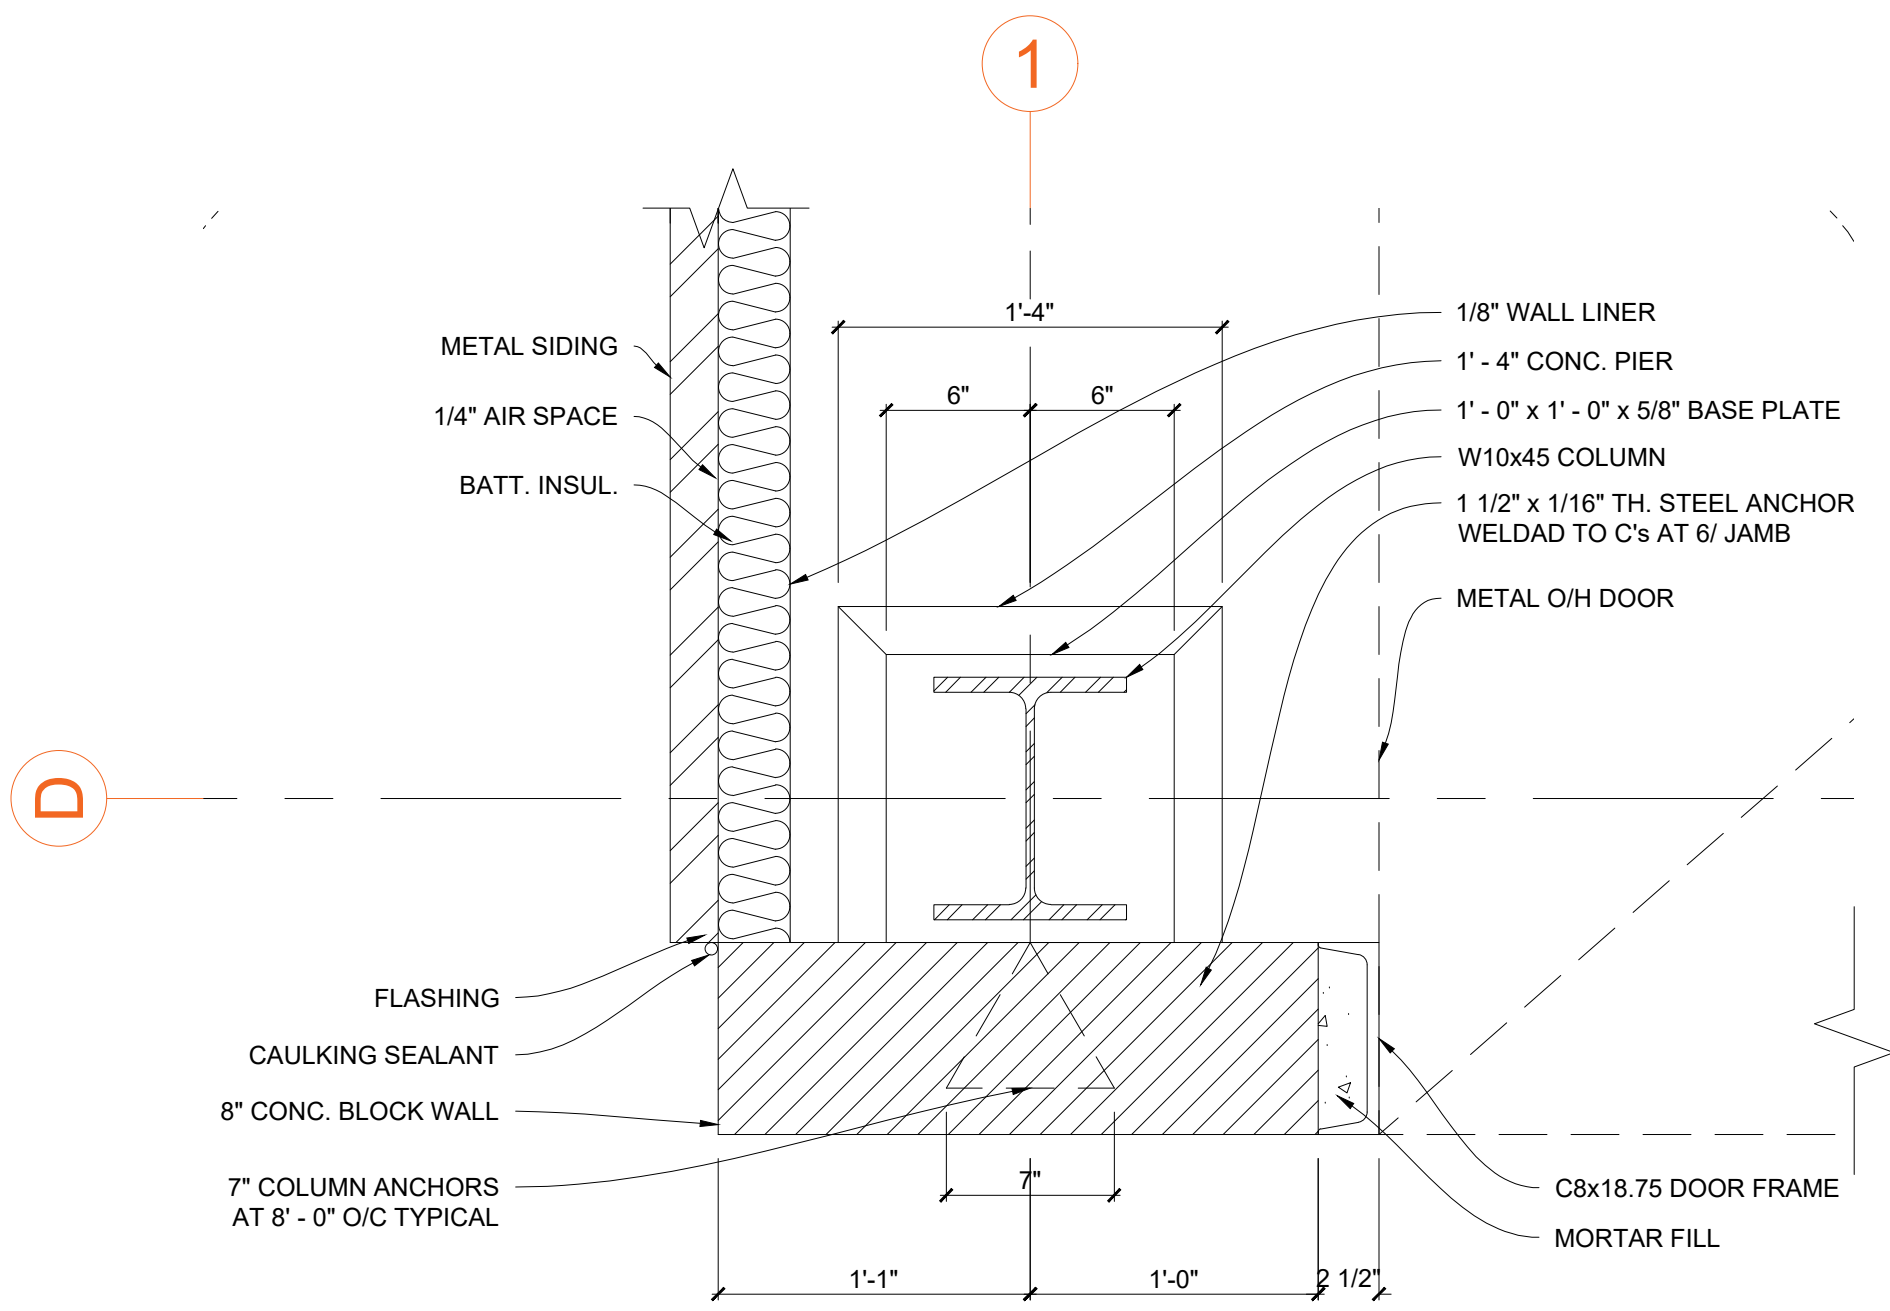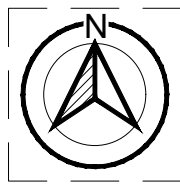

3 COLUMN D1 DETAIL
SCALE: 1 - 1/2" = 1' - 0"

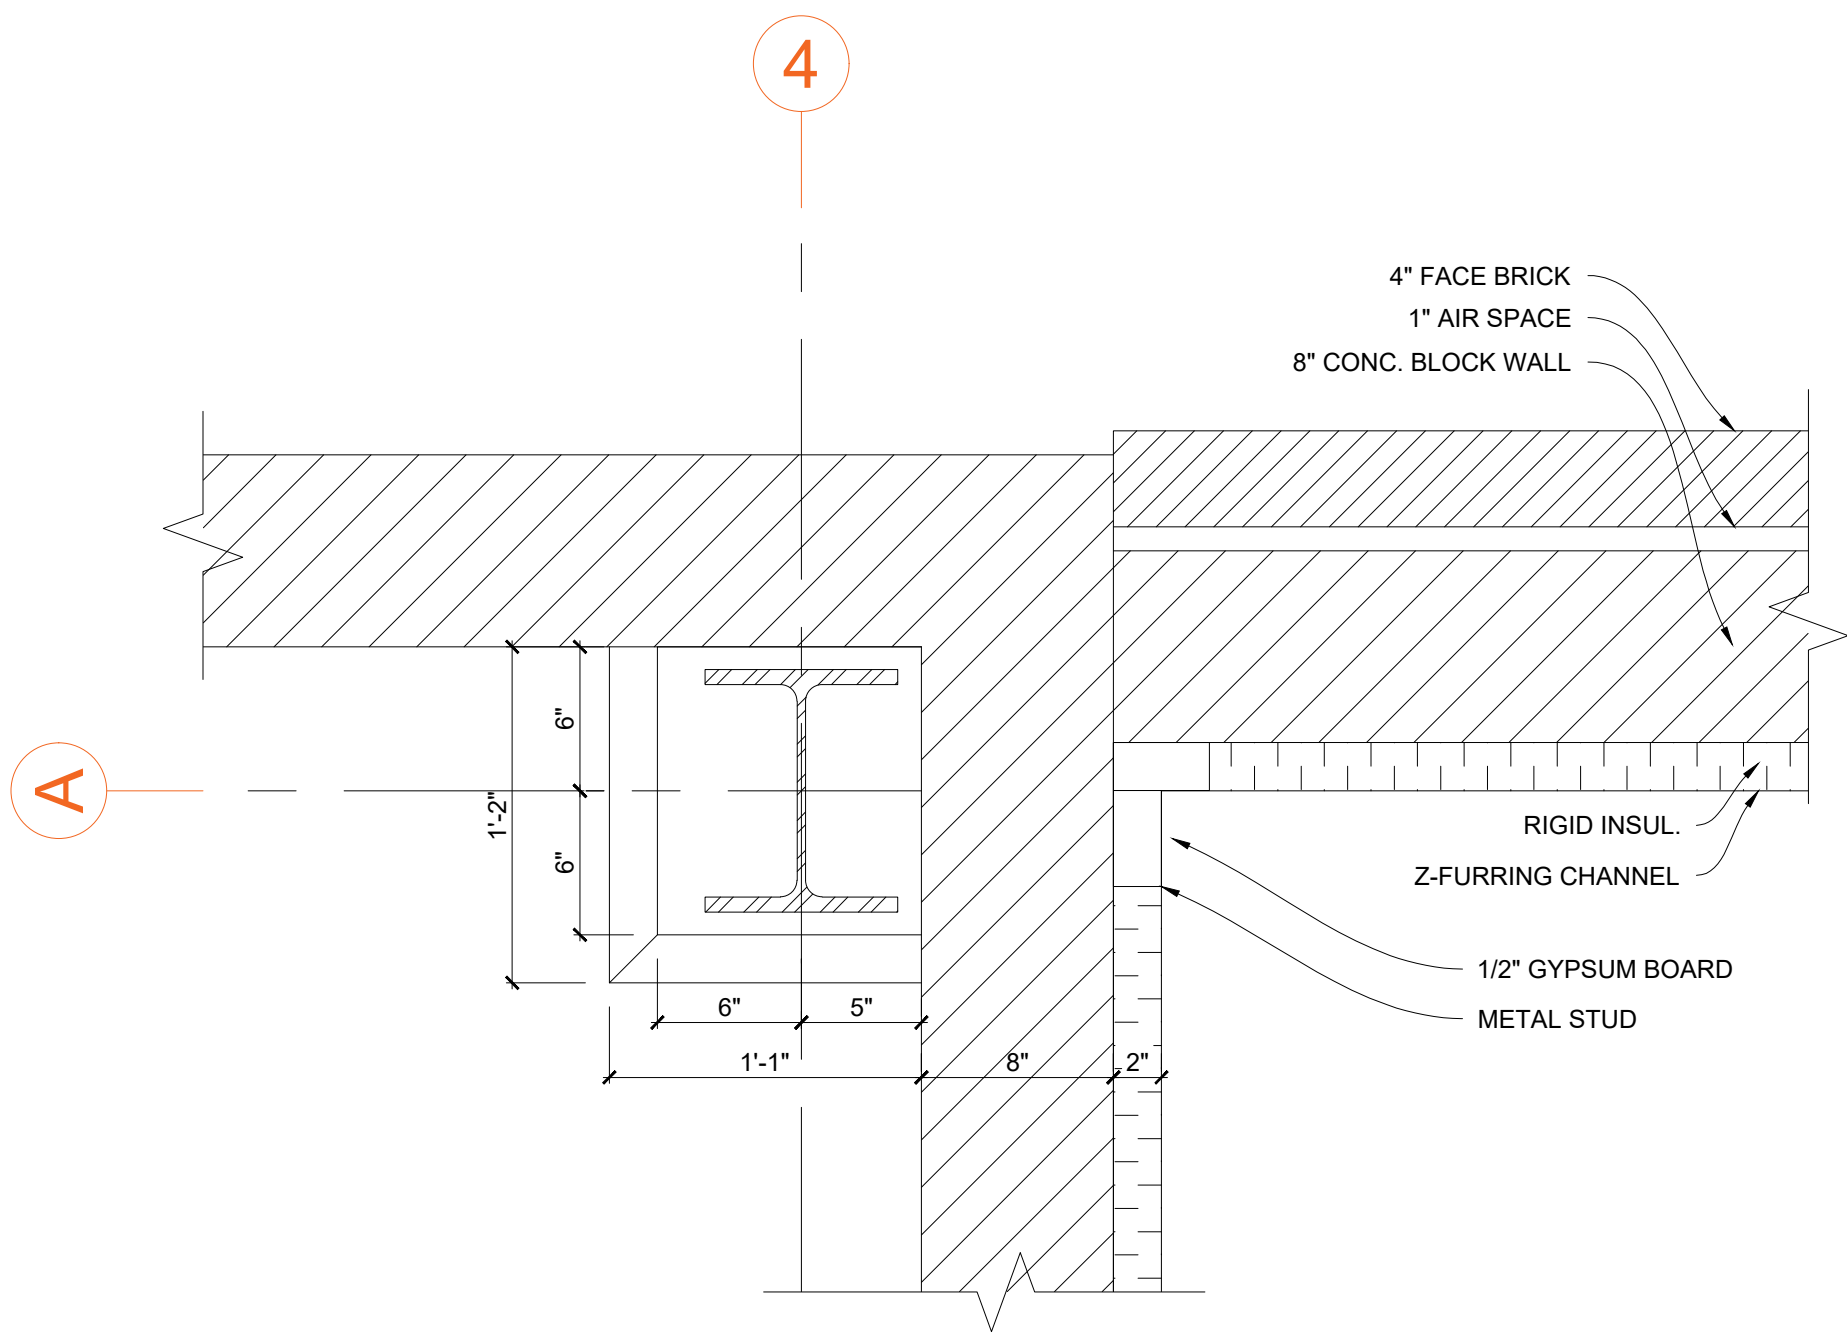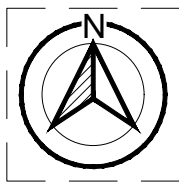

4 COLUMN A4 DETAIL
SCALE: 1 - 1/2" = 1' - 0"

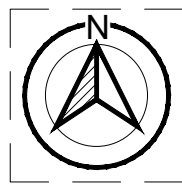

Project Title:
SHOP & OFFICE

Drawing Title:
FLOOR PLAN DETAILS

Drawing By: Bruno Arriola
Checked By: Jie Zhang
Scale: SCL
Date: 10.17.2025

Drawing No.: AS
Sheet No.: A2.2